





DESIGN ANALYSIS

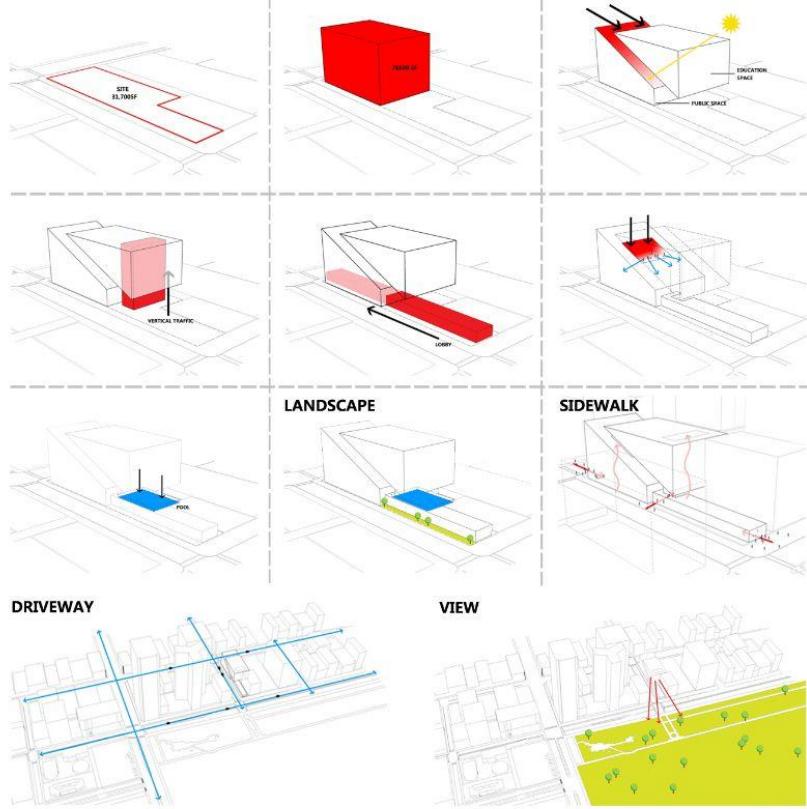



BALANCE

when I look things about dancer, I found the most important thing is balance. So choose balance as my concept. I divided the space into two parts, theater and education space. To make the two space to keep balance.

SITE

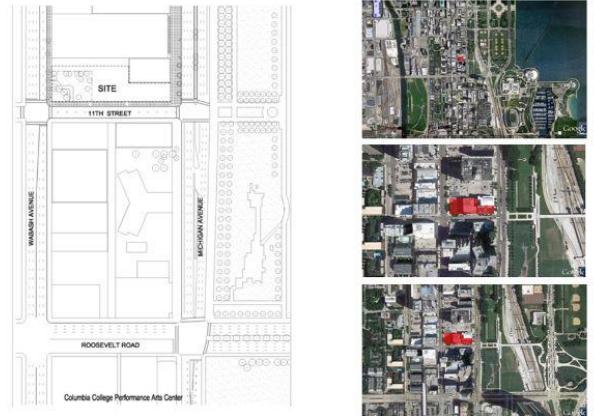


FUNCTION

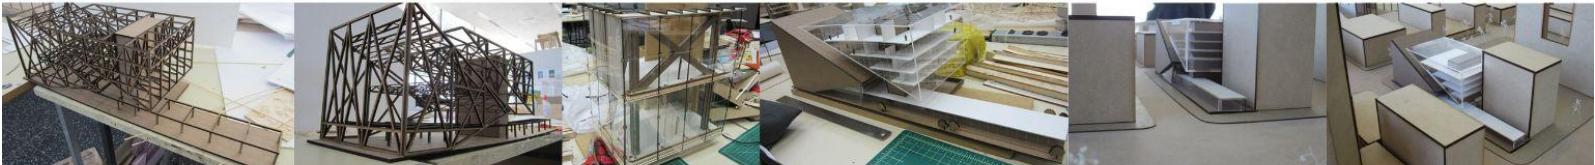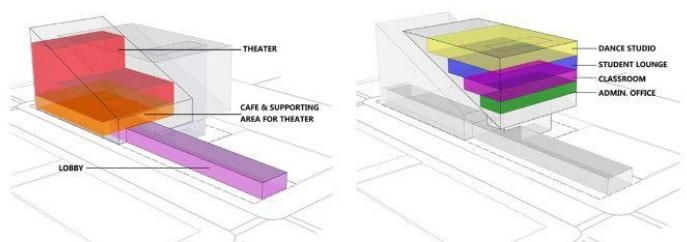



ROOF PLAN

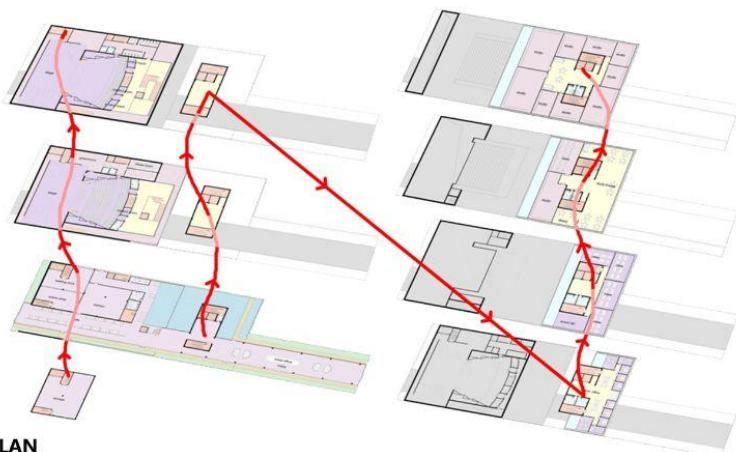




GROUND PLAN



NORTH ELEVATION



SOUTH ELEVATION

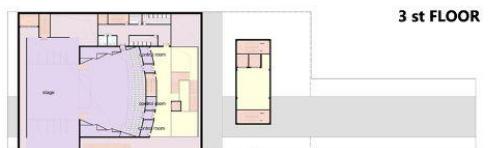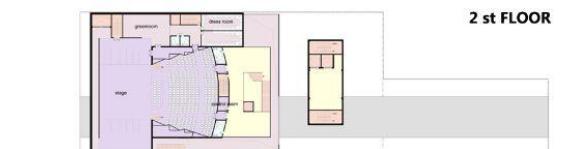
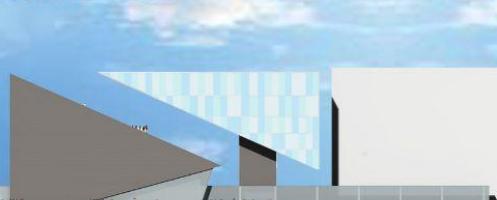


EAST ELEVATION




WEST ELEVATION




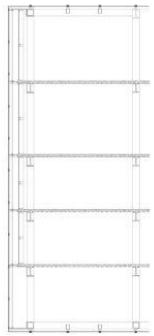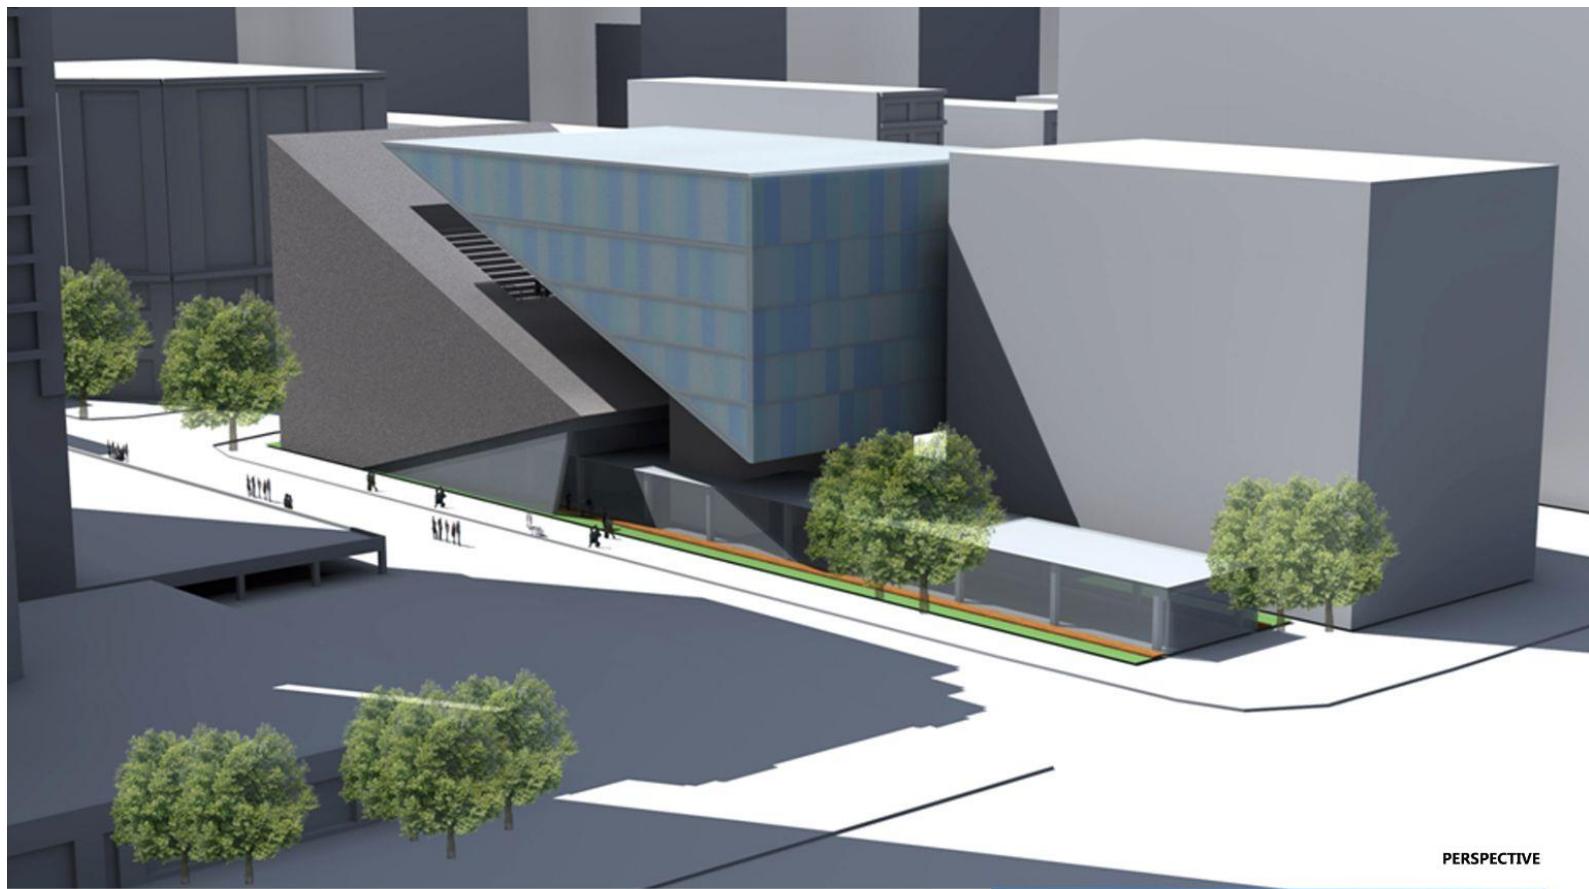

WALL SECTION DETAIL 1


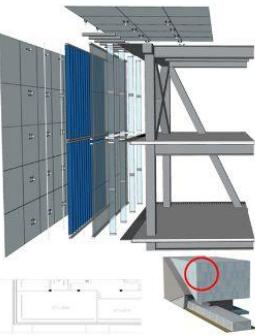


WALL SECTION DETAIL 2



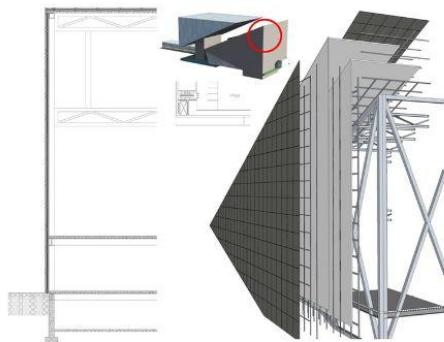


A-A SECTION

B-B SECTION

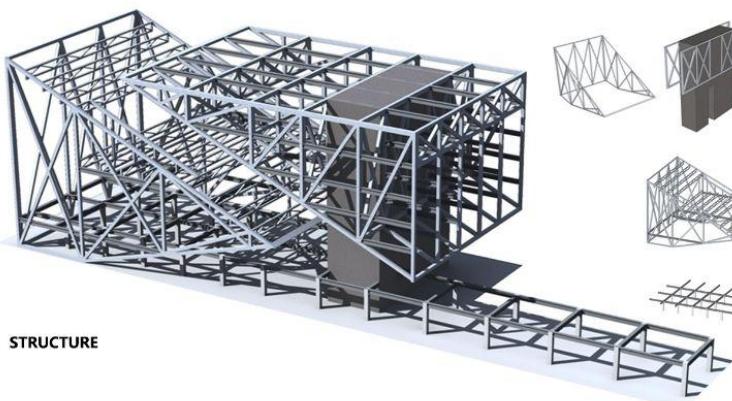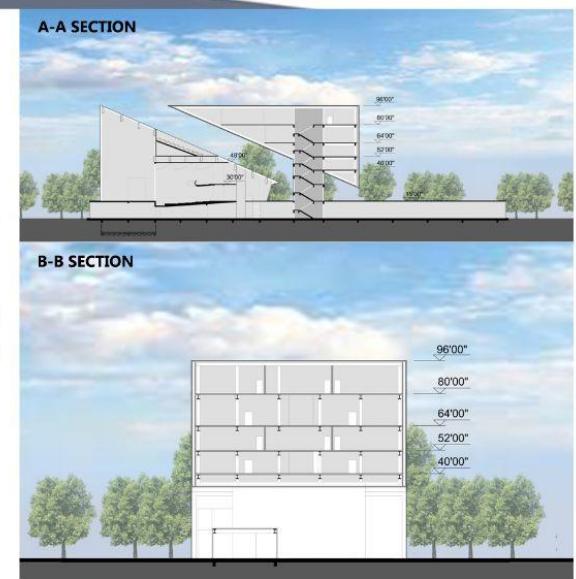

STRUCTURE

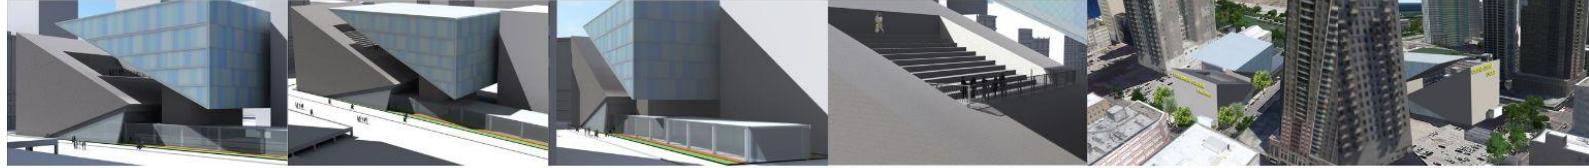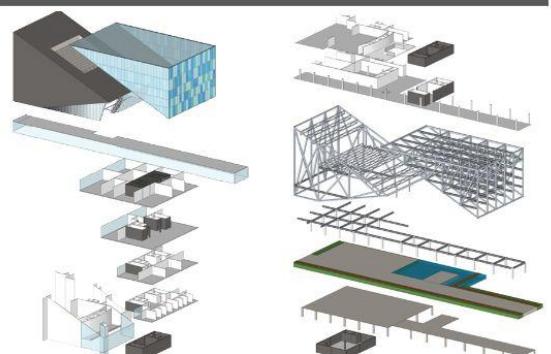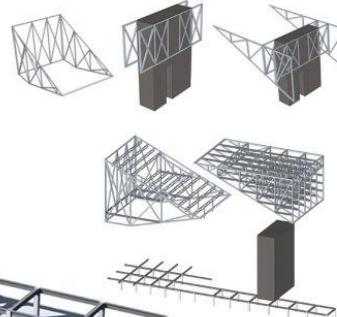


DANCE / PERFORMING ARTS CENTER- CHICAGO

BIKE CENTER DESIGN




Analysis

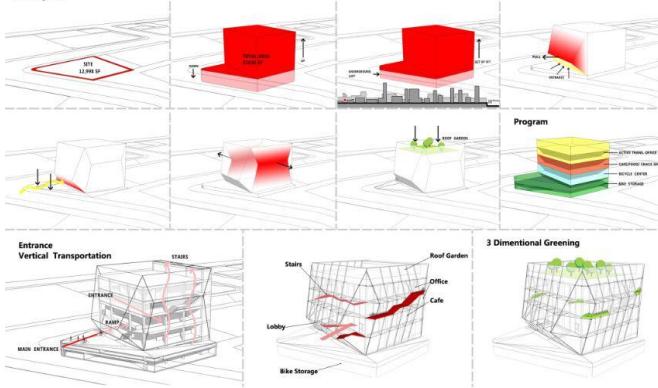

This program is separated into Bicycle related program (public) and Active Trans. Program. I want to make this building to be a rectangle box, at this way can open the entrance of the building to be a large public plaza. After analysis the program, found the connection of different party, then make stairs between the related function along with the form of the facade. Cover the center box with a transparent glass box, make the building have a double facades.




Wall Section

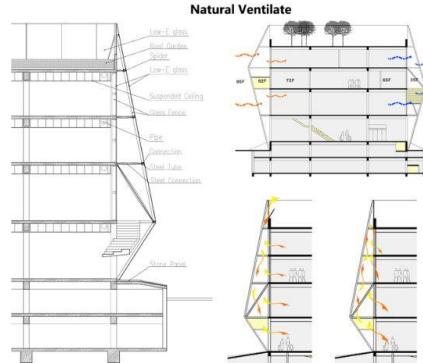


Facades











A-A Section 1/16"

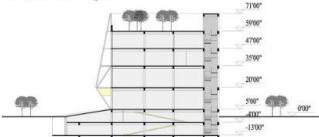




B-B Section 1/16"

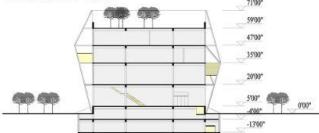



BIKE CENTER DESIGN

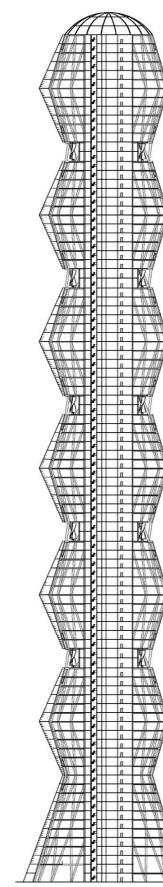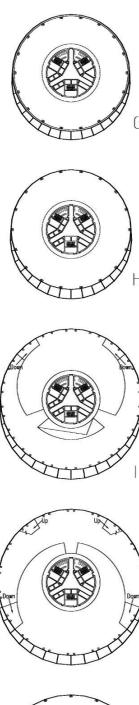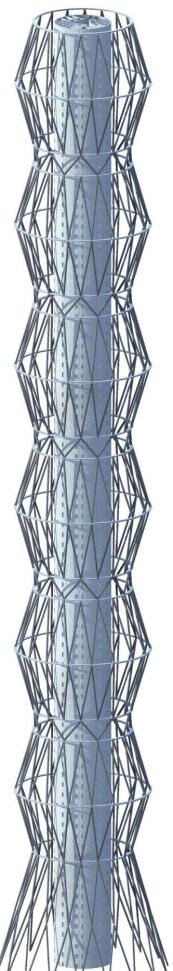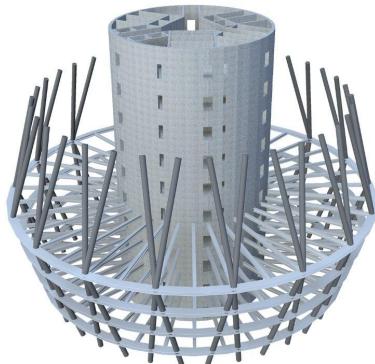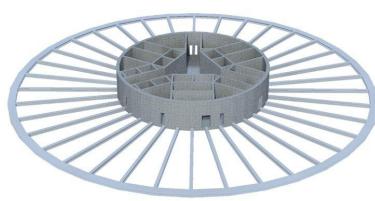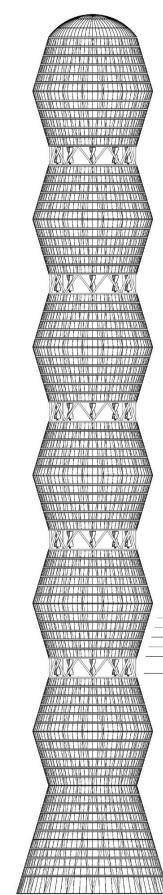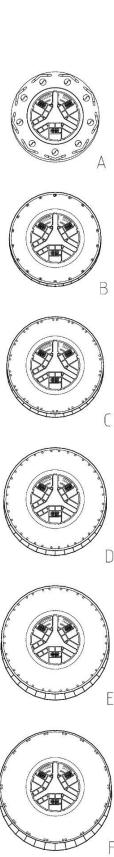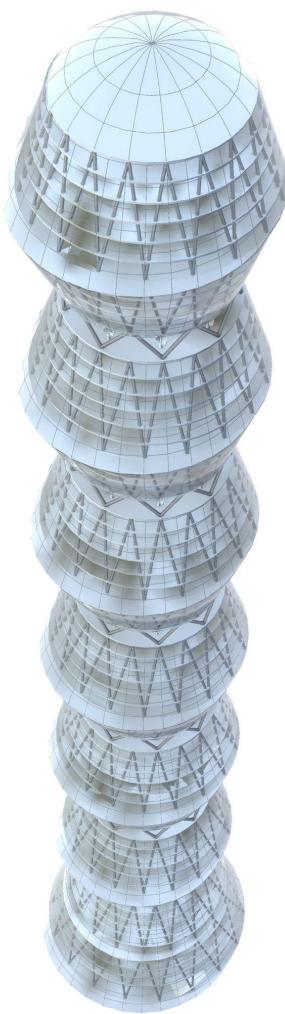


Wind Energy High-rise

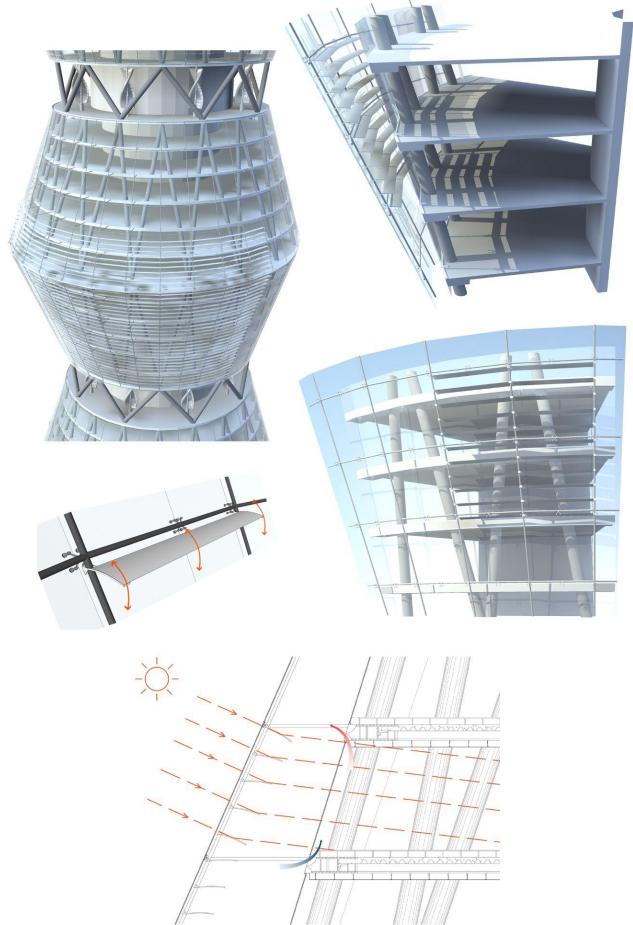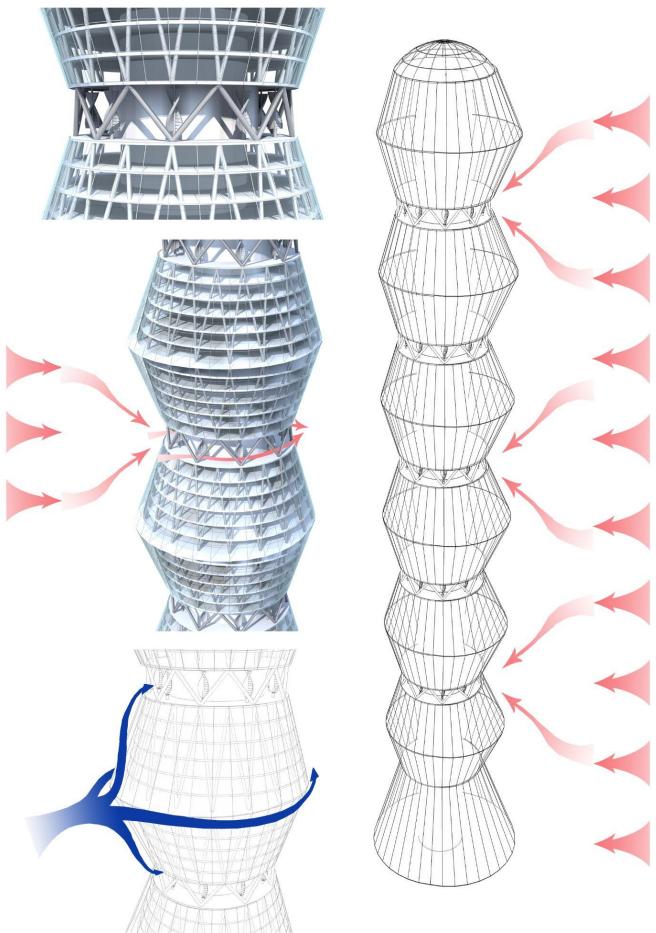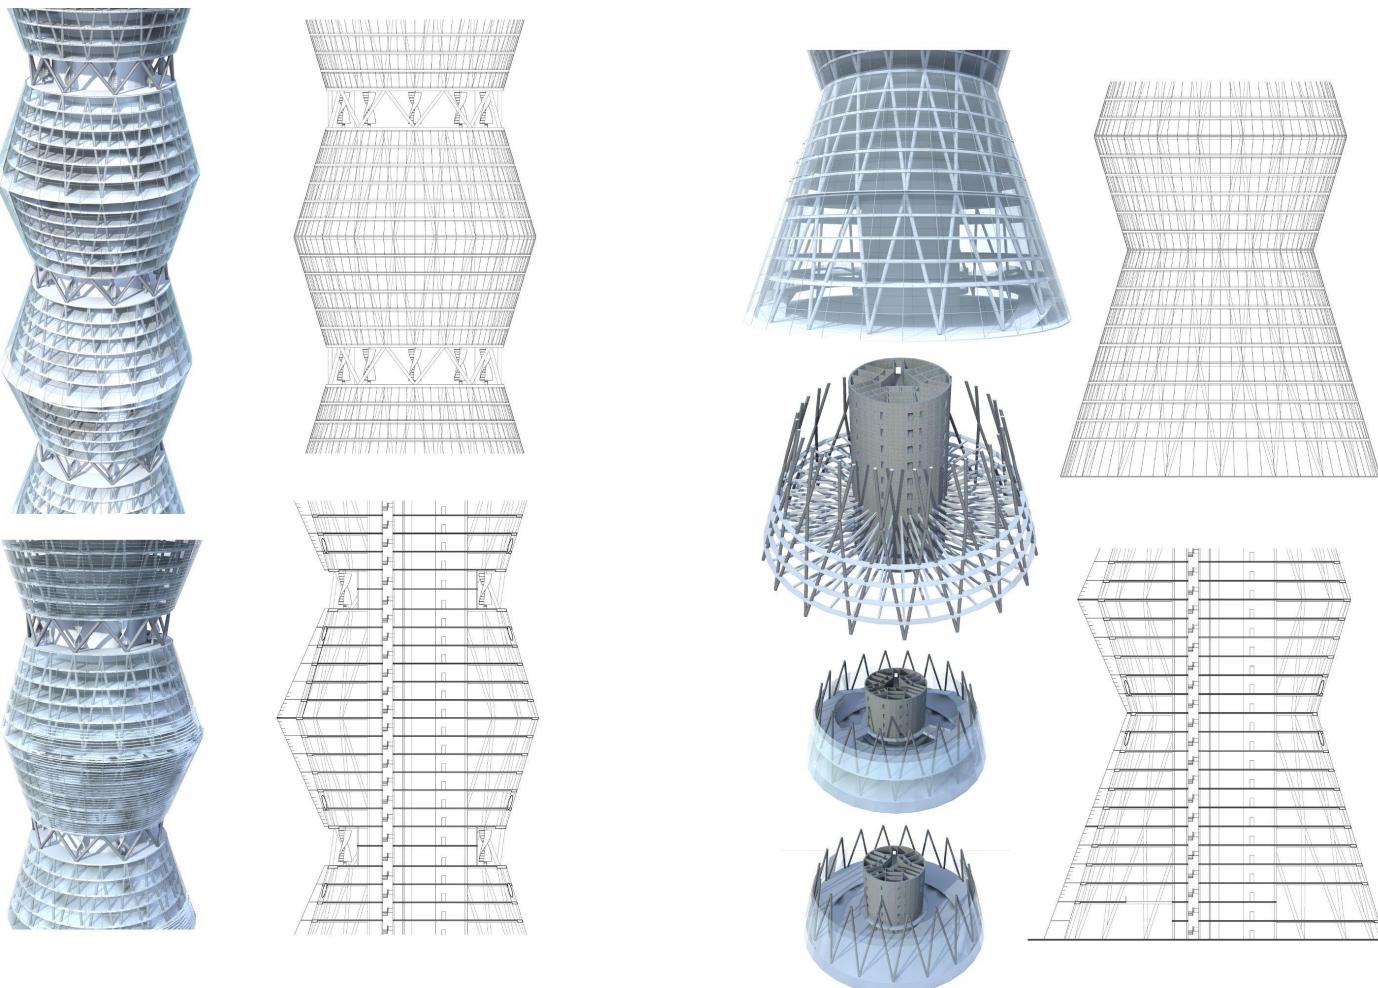



Wind Energy High-rise

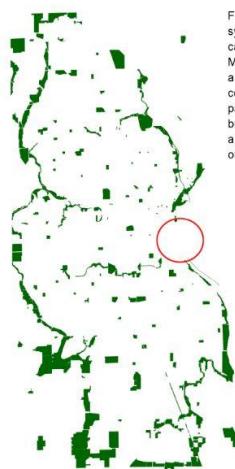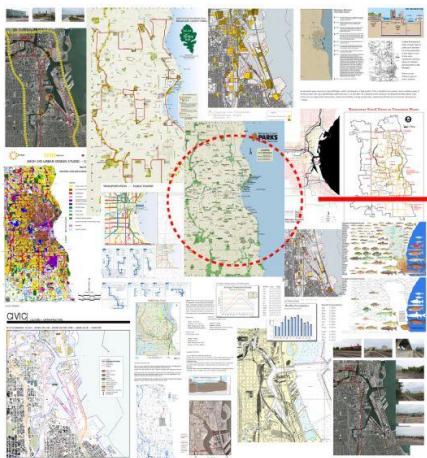


From the park system, we can find Milwaukee has a large and continuous park system, but there has a gap just in our site.

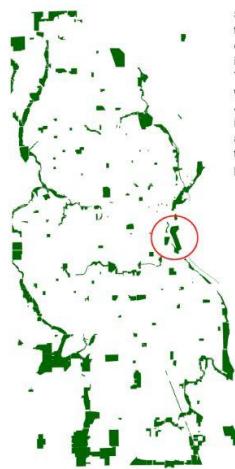


So I try to fill this gap by design a park in my site. Then that's why I add Jones Island into my site, and make it to be a large park.

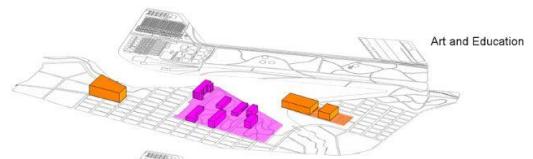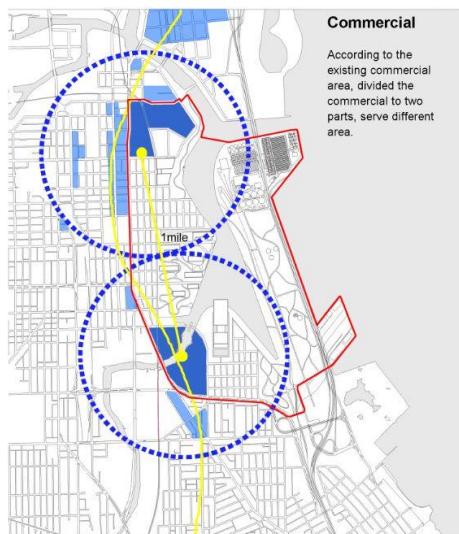

Art and Education

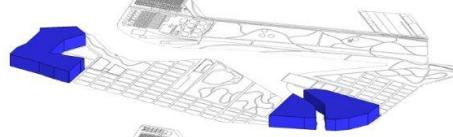


Commercial

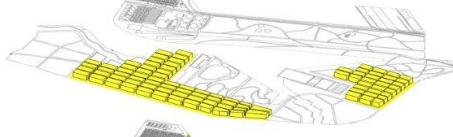


Residential



Park

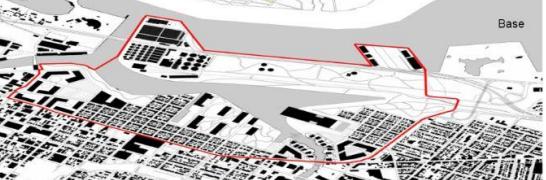

Base

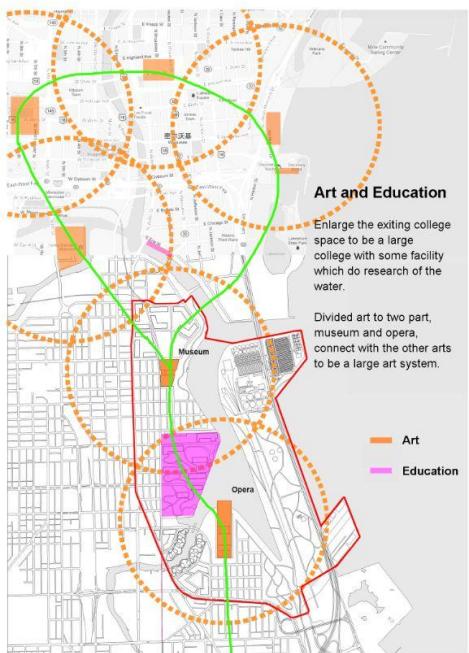


CITY CONFLUENCE



Park

Sports Park 1:1000

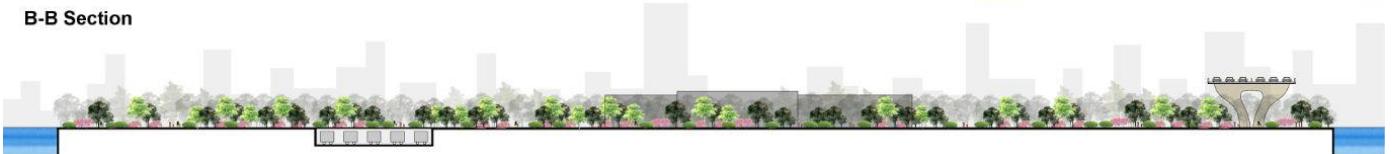

CITY CONFLUENCE

Detail Plan 1:1000

Opera



CITY CONFLUENCE



CITY CONFLUENCE